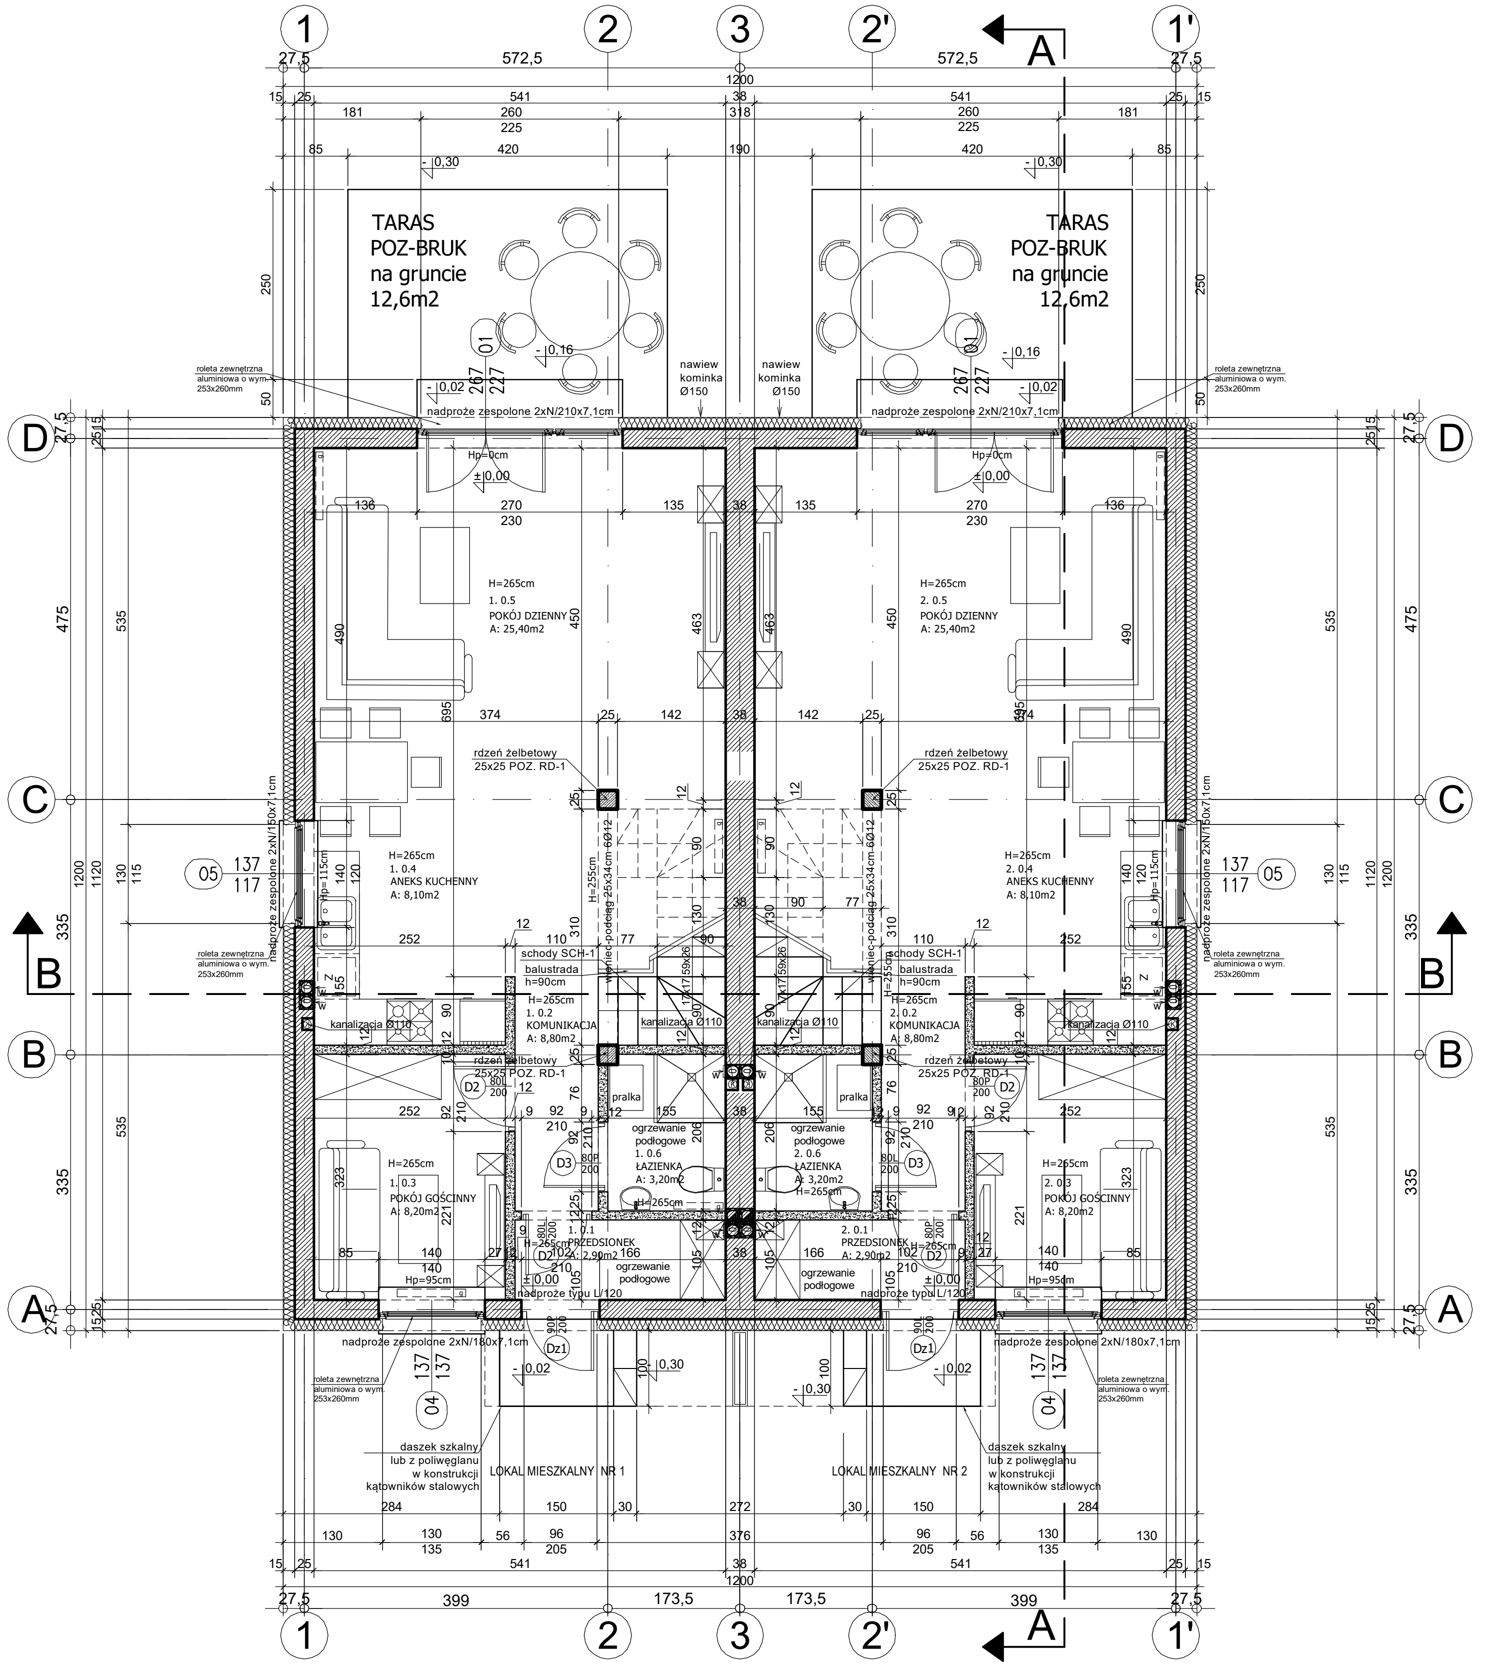
1
2
3
2'
1'
A
B
C
D
27,5
572,5
1200
541
38
318
260
225
181
85
420
190
- 0,30
TARAS
POZ-BRUK
na gruncie
12,6m2
250
01
267
227
- 0,16
- 0,02
50
nawiew
kominka
Ø150
roleta zewnętrzna
aluminiowa o wym.
253x260mm
nadproże zespolone 2xN/210x7,1cm
Hp=0cm
± 0,00
270
230
135
136
H=265cm
1. 0.5
POKÓJ DZIENNY
A: 25,40m2
2. 0.5
490
450
463
475
535
695
374
142
25
rdzeń żelbetowy
25x25 POZ. RD-1
nadproże zespolone 2xN/150x7,1cm
05
137
117
H=265cm
1. 0.4
ANEKS KUCHENNY
A: 8,10m2
2. 0.4
Hp=115cm
140
120
130
115
1120
335
wieniec-podciąg 25x34cm 6Ø12
H=255cm
310
90
77
110
252
12
schody SCH-1
balustrada
h=90cm
H=265cm
1. 0.2
KOMUNIKACJA
A: 8,80m2
2. 0.2
17x17,59x26
kanalizacja Ø110
D2
80L
200
80P
pralka
ogrzewanie
podłogowe
1. 0.6
ŁAZIENKA
A: 3,20m2
2. 0.6
H=265cm
D3
155
206
210
92
H=265cm
1. 0.3
POKÓJ GOŚCINNY
A: 8,20m2
2. 0.3
323
221
1. 0.1
PRZEDSIONEK
A: 2,90m2
2. 0.1
166
105
102
Hp=95cm
nadproże typu L/120
nadproże zespolone 2xN/180x7,1cm
90P
90L
Dz1
04
137
100
0,30
- 0,02
daszek szkalny
lub z poliwęglanu
w konstrukcji
kątowników stalowych
LOKAL MIESZKALNY NR 1
LOKAL MIESZKALNY NR 2
284
150
30
272
130
56
96
376
135
205
399
173,5
15
25