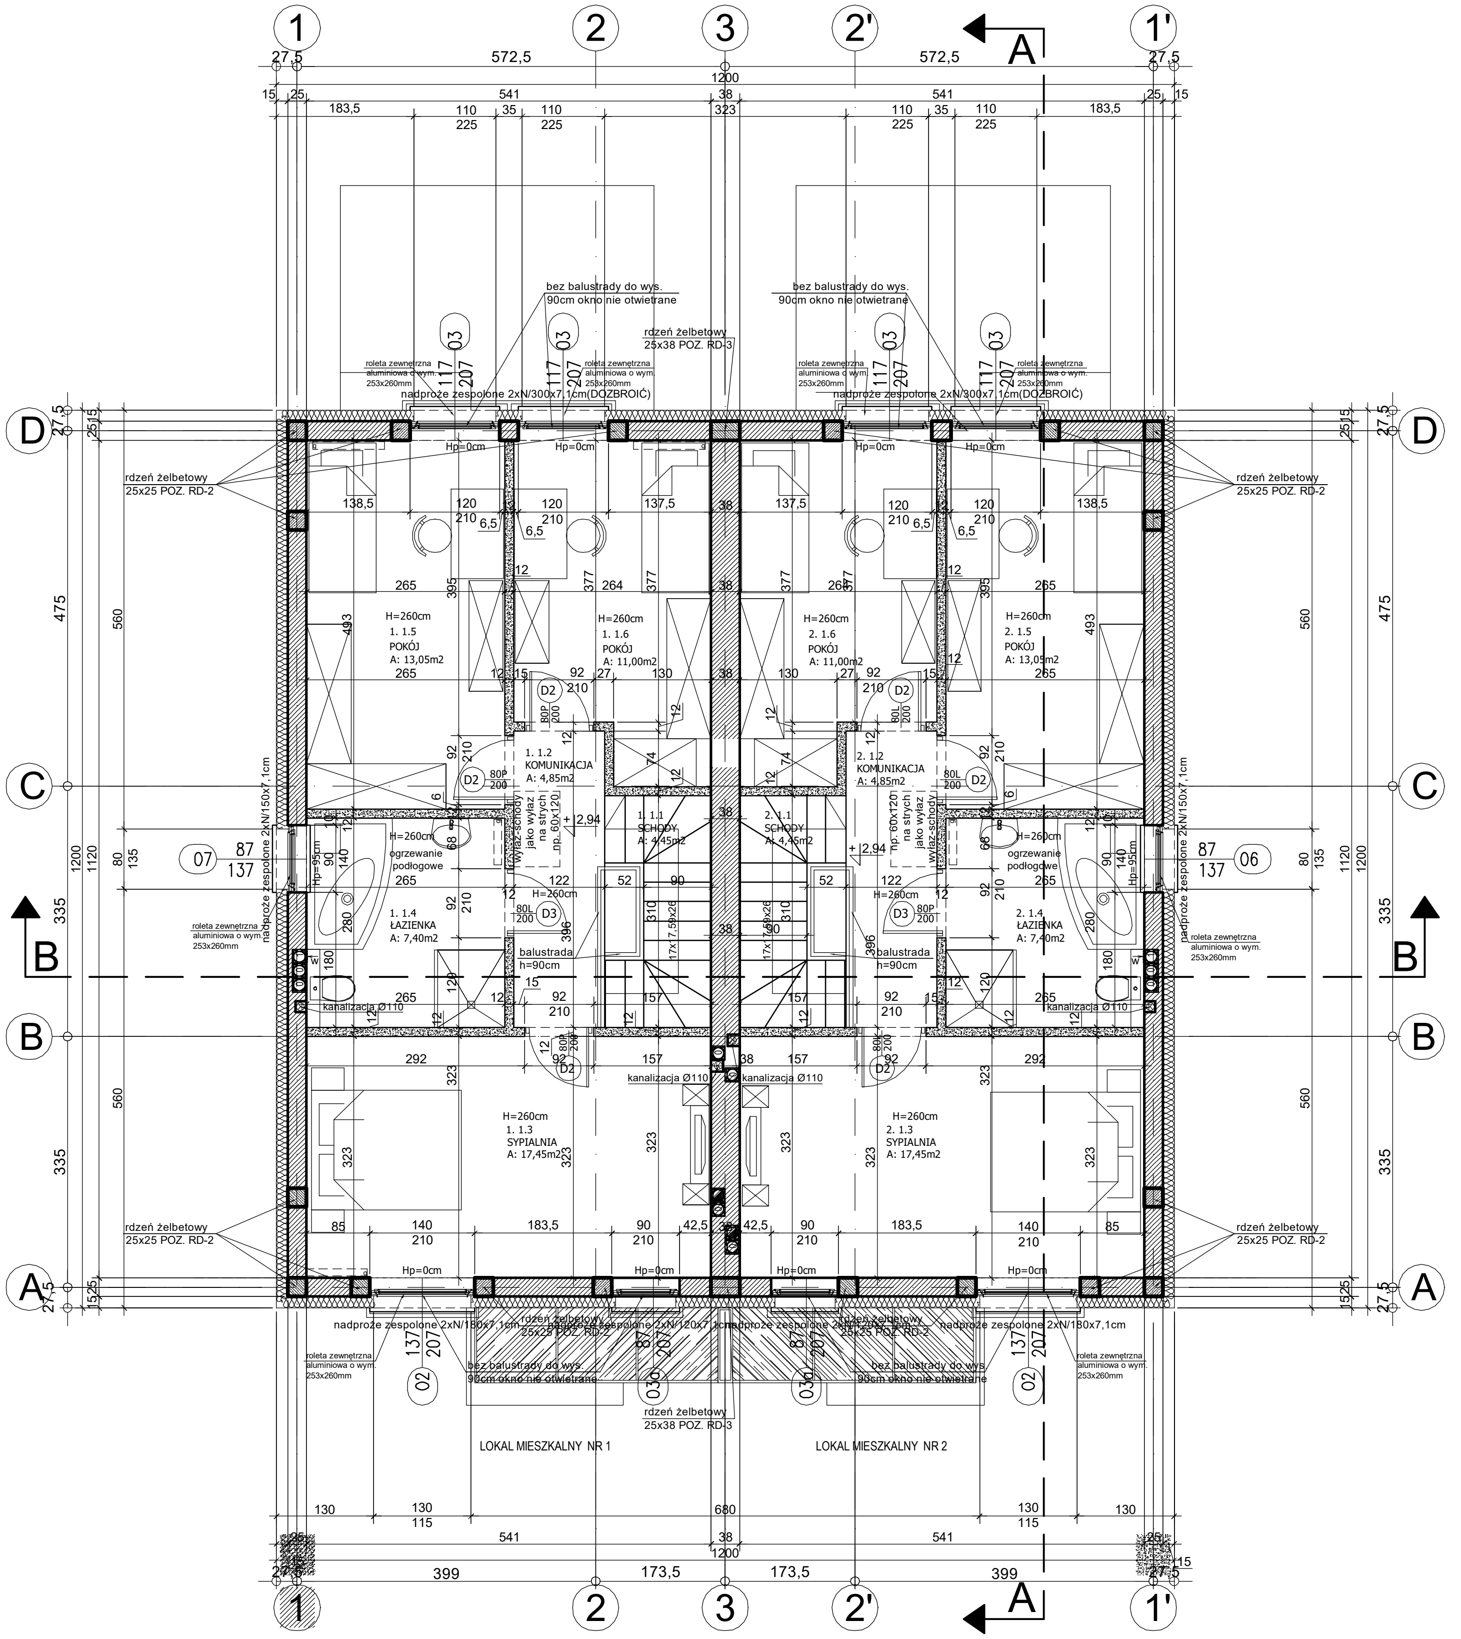

1
2
3
2'
1'
A
B
C
D
572,5
1200
541
38
183,5
110
225
35
323
bez balustrady do wys. 90cm okno nie otwietrane
rdzeń żelbetowy 25x38 POZ. RD-3
rdzeń żelbetowy 25x25 POZ. RD-2
roleta zewnętrzna aluminiowa o wym. 253x260mm
nadproże zespolone 2xN/300x7,1cm(DOZBROIĆ)
nadproże zespolone 2xN/150x7,1cm
nadproże zespolone 2xN/180x7,1cm
nadproże zespolone 2xN/120x7,1cm
03
117
207
02
137
030
87
07
06
Hp=0cm
Hp=95cm
H=260cm
1. 1.5
POKÓJ
A: 13,05m2
1. 1.6
POKÓJ
A: 11,00m2
2. 1.6
POKÓJ
A: 11,00m2
2. 1.5
POKÓJ
A: 13,05m2
1. 1.2
KOMUNIKACJA
A: 4,85m2
2. 1.2
KOMUNIKACJA
A: 4,85m2
1. 1.1
SCHODY
A: 4,45m2
2. 1.1
SCHODY
A: 4,45m2
1. 1.4
ŁAZIENKA
A: 7,40m2
2. 1.4
ŁAZIENKA
A: 7,40m2
ogrzewanie podłogowe
1. 1.3
SYPIALNIA
A: 17,45m2
2. 1.3
SYPIALNIA
A: 17,45m2
wyłaz-schody jako wyłaz na strych np. 60x120
+2,94
balustrada h=90cm
17x 7,58x26
D2
D3
80P
80L
200
kanalizacja Ø110
LOKAL MIESZKALNY NR 1
LOKAL MIESZKALNY NR 2
475
560
335
1120
135
80
27,5
15
25
130
115
680
399
173,5